


FTTH - LLD NETWORK DESIGN PHASE 6 DHA

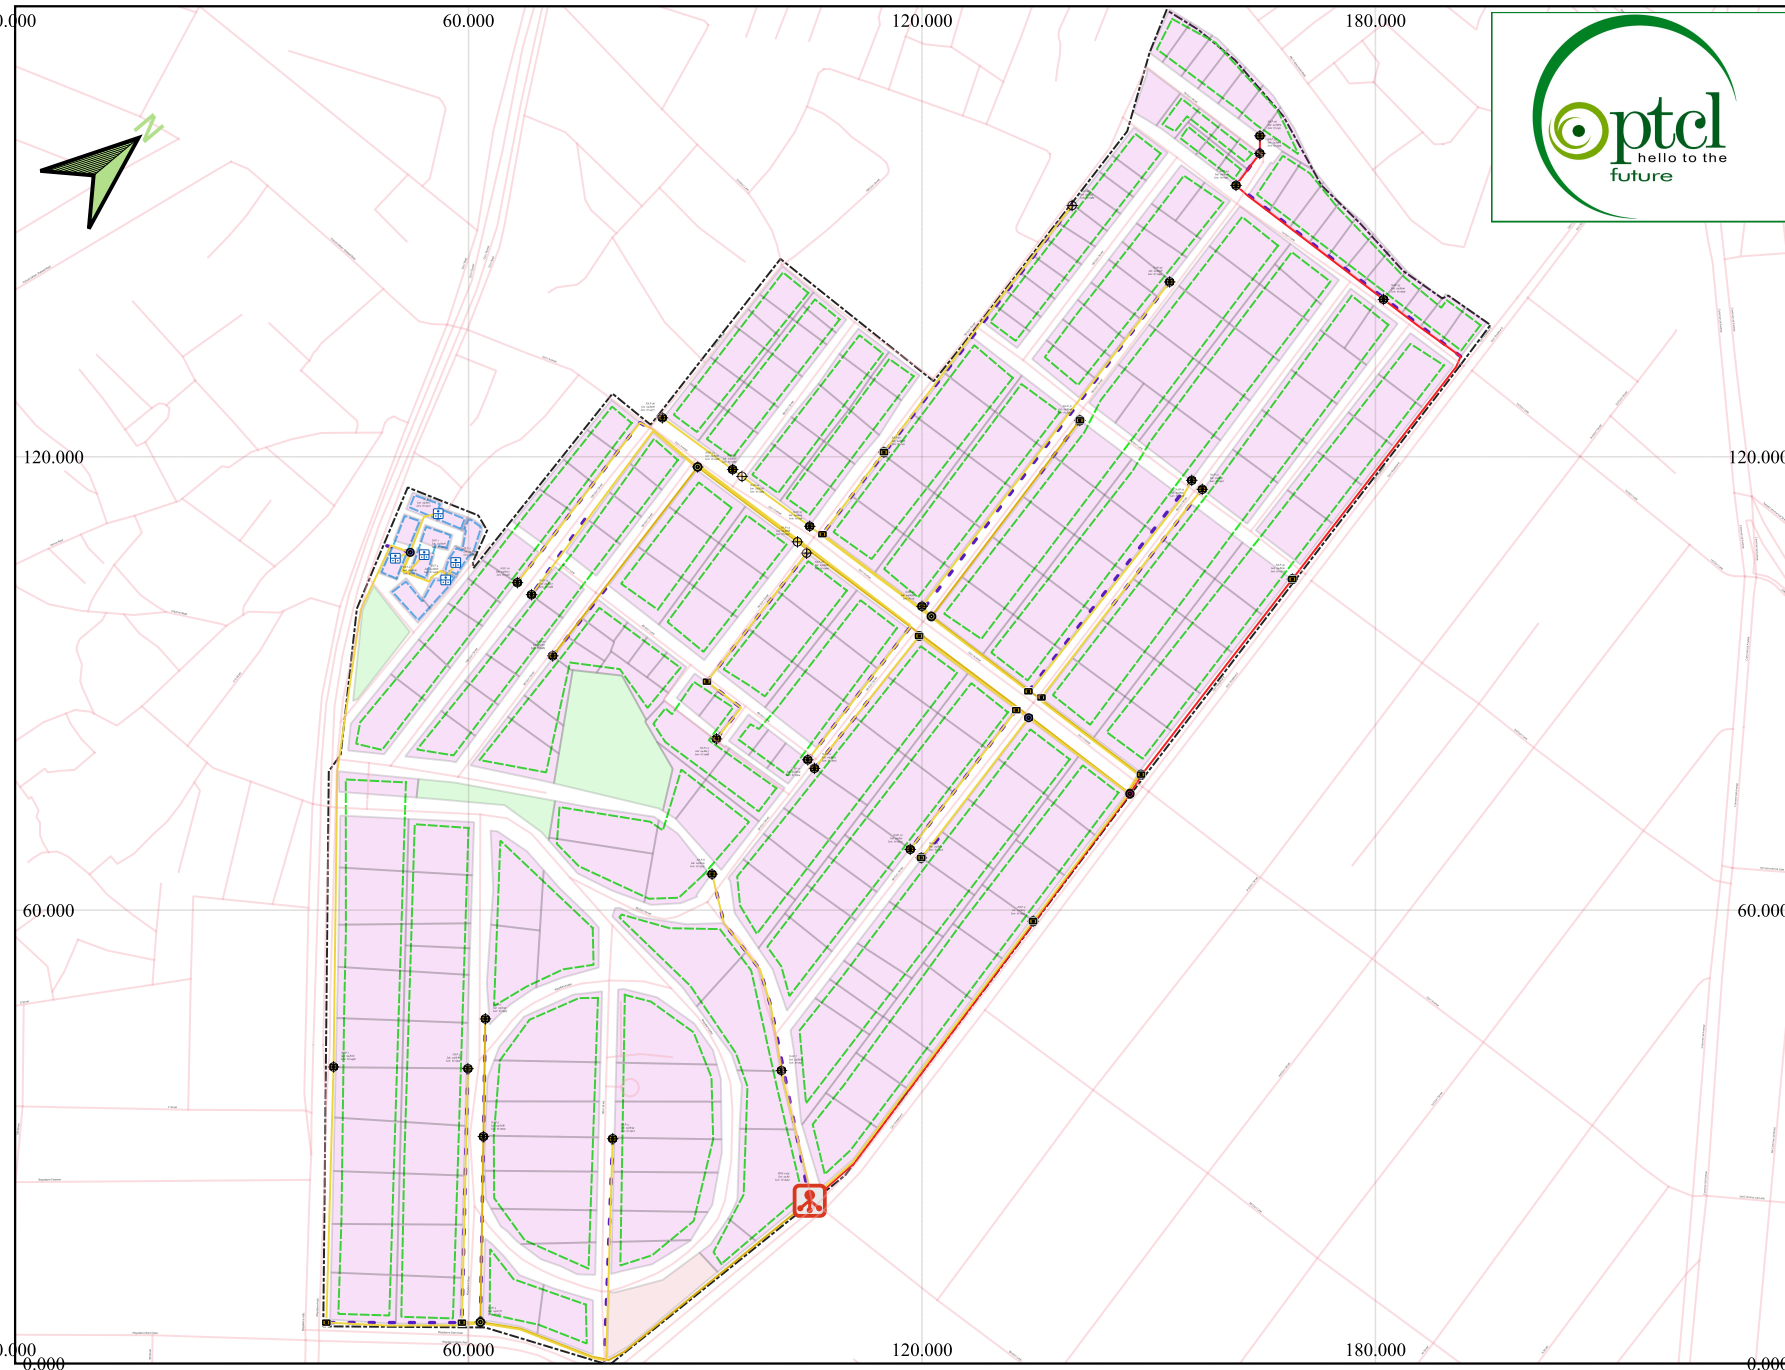

Legend

Distribution_Splice_Closures

- 12F
- 24F
- 48F

DKTCC_Structure

- HandHole
- highway

Units

- FAT
- FDH
- ⊕ NAP

New_Structure

- HandHole
- ManHole

Distribution_Cables

- 12F
- 24F
- 48F

New_Planned_Ducts

- 1 way

Basemap

- CMO Tower
- Consumer
- Public Amuney

Boundary

- FAT Boundary
- FDH Boundary
- NAP Boundary

0 0.1 0.2 km

LLD - NETWORK SUMMARY

FDH Name: 1005 Distribution Cable: 7.70 km
Distribution Duct: 2.51 km NAP: 36 FAT: 5 Splice Closure: 6

Prepared By:
Abdullah Aweem
Network & GIS Specialist

Coordinate System:
WGS 84 / UTM Zone 32N
EPSG:32632