


SERVICEABILITY MAP

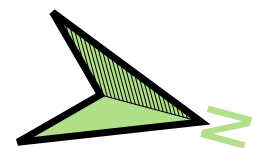

Legend

Distribution_Splice_Closures

- 12F
- 24F
- 48F

Units

- FAT
- FDH
- NAP

Distribution_Cables


- 12F
- 24F
- 48F

Basemap

- CMO Tower
- Consumer
- Public Amunity

Boundary

- FAT Boundary
- NAP Boundary

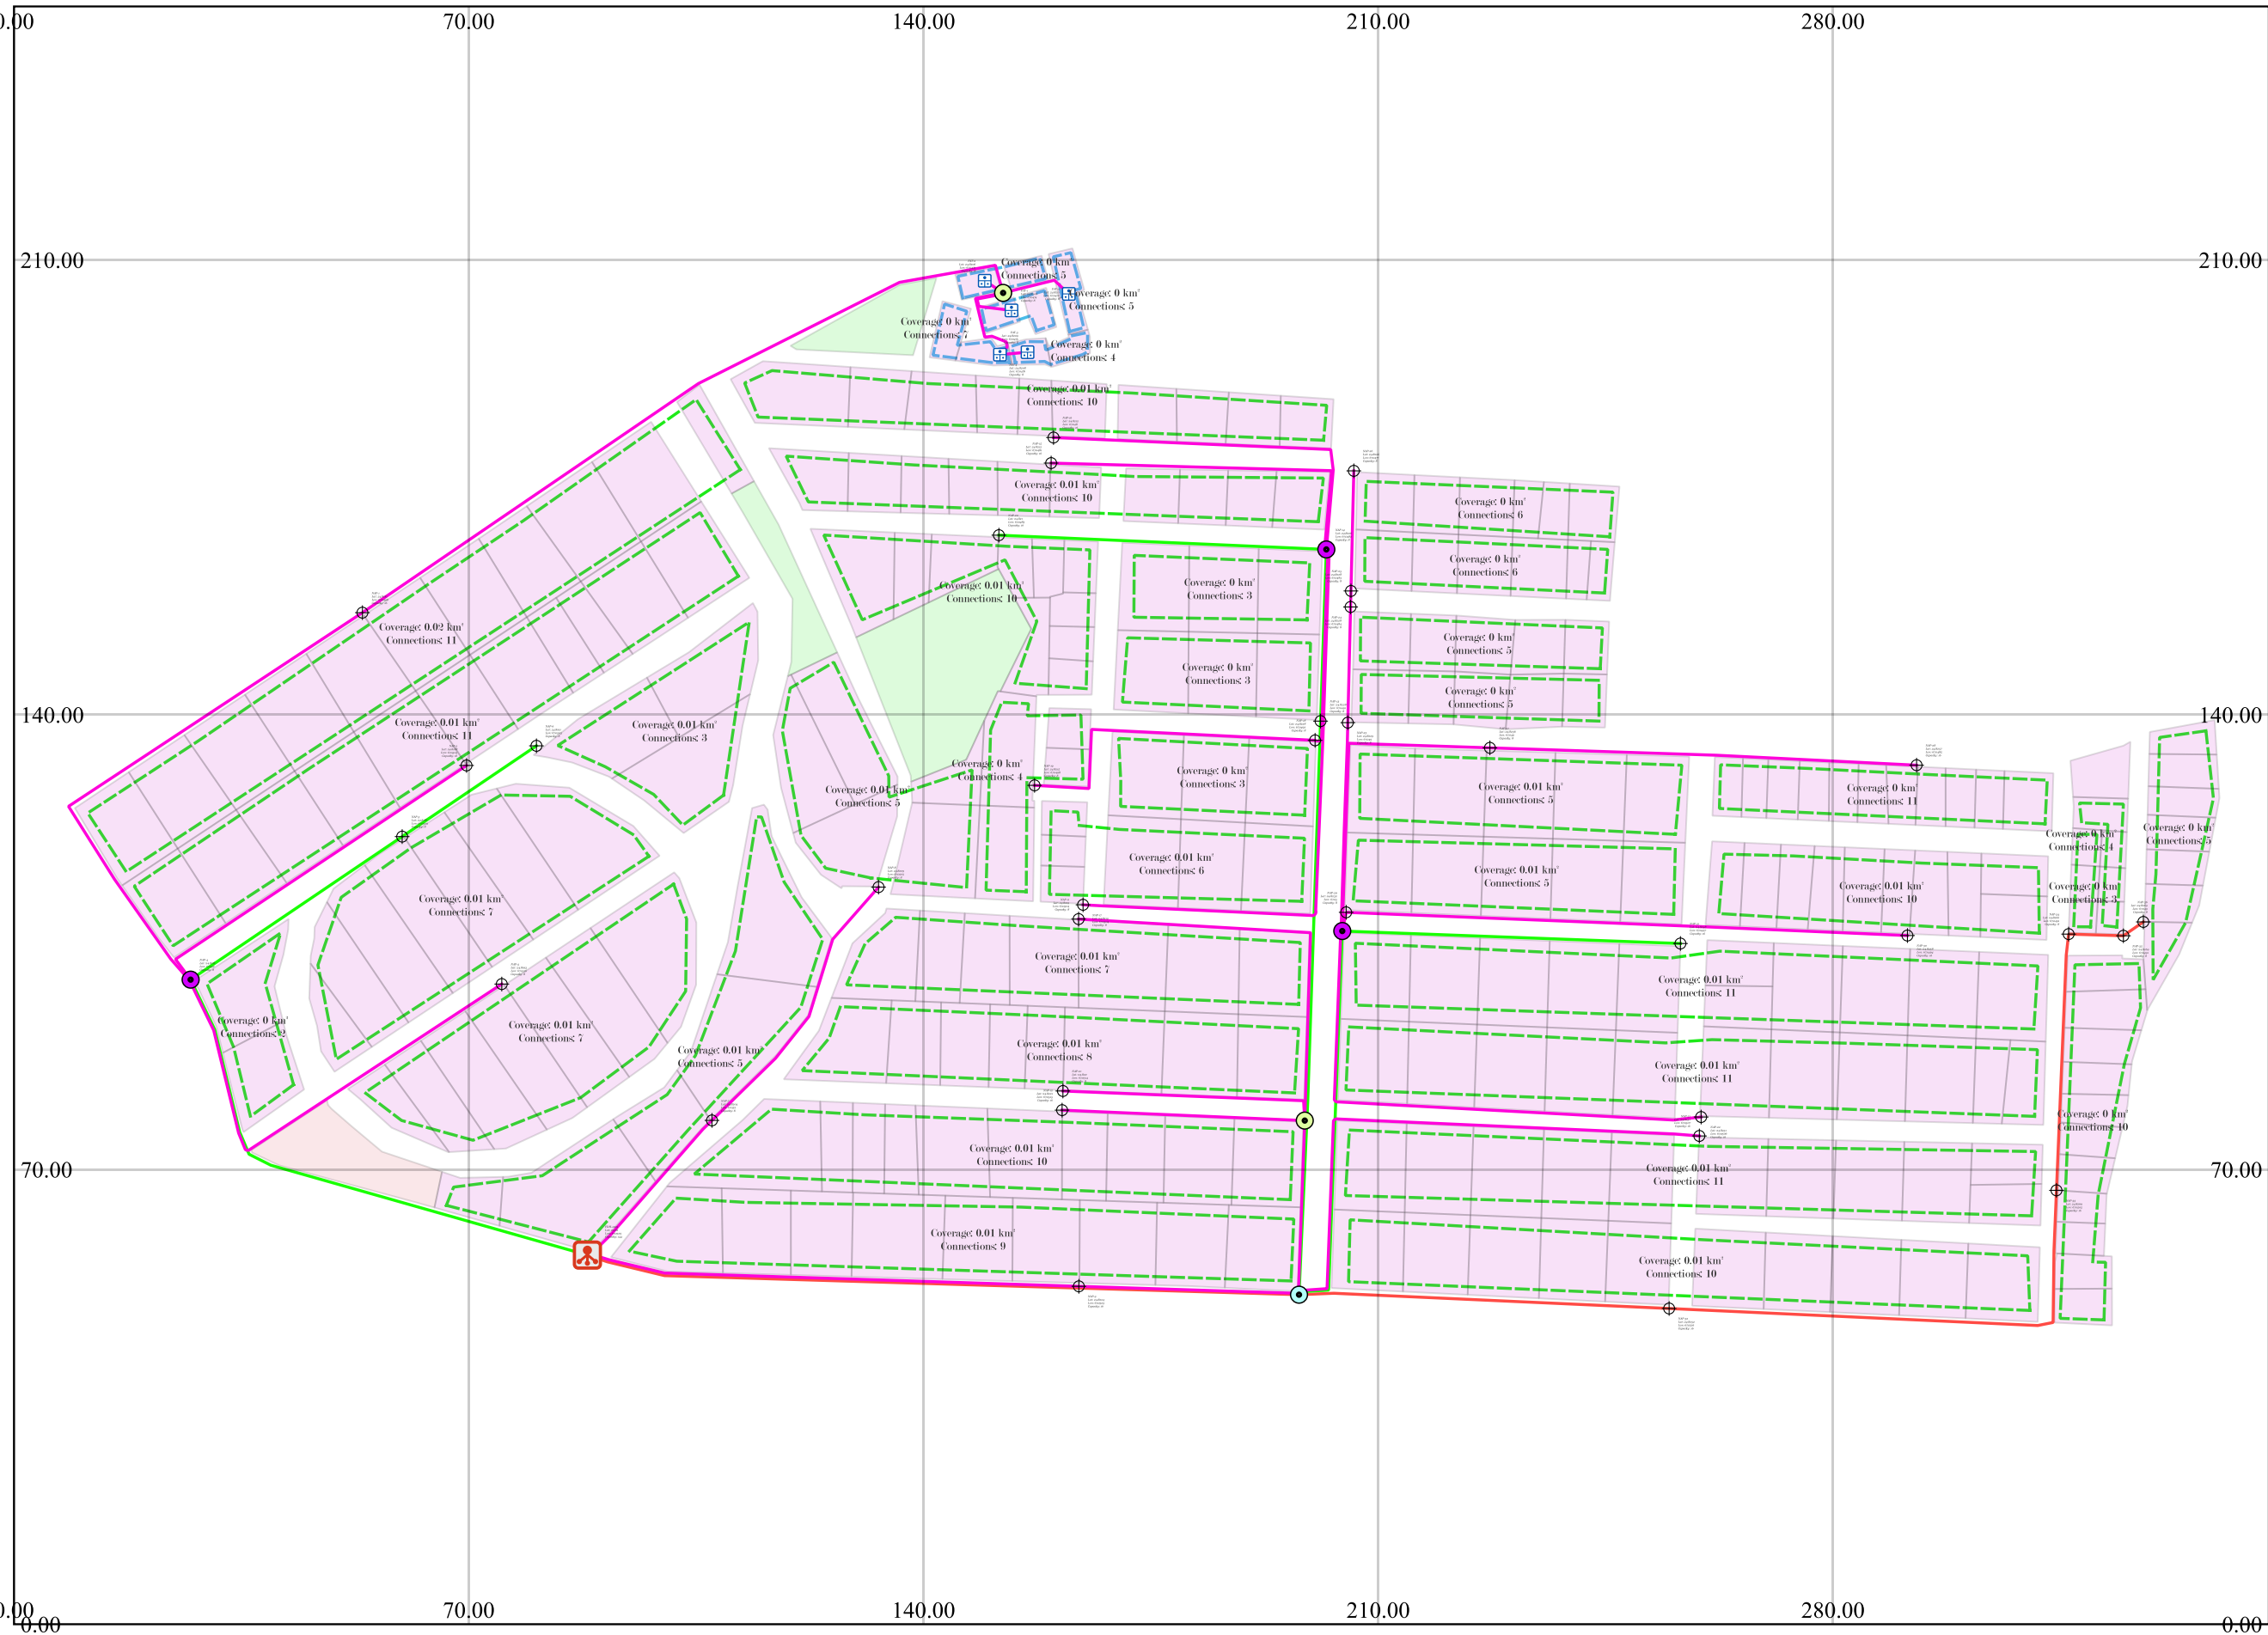

FDH: 1005/144 Status: Planned
NAP: 36 , FAT: 5 , Splice Closure: 6
Capacity: 8/16 Capacity: 8/16 Capacity: 12F/24F/48F
Residential/Commercial: 257/5 , Connection: 264/13

Prepared By:
Abdullah Aweem
Network & GIS Specialist

Coordinate System:
WGS 84 / UTM Zone 32N
EPSG: 32632